PACHET COMPLET R03

Plan general al parcelei + curte și accese + subsol + parter + etaj

Pachetul reunește toate componentele discutate într-o singură propunere pentru arhitect. Planurile sunt orientate cu nordul în sus. Strada General Drăgălina este la est/dreapta, iar strada Cloșca la sud/jos.

Cuprins

1–2	Tema generală, coordonarea nivelurilor și lista de verificări.
3–4	Plan general C01: parcela, curtea, acces pietonal Dragalina, acces auto Cloșca, poarta la 90°, două parcări și traseele spre apartamente/beci.
5–7	Subsol S09: plan, secțiune longitudinală și secțiune transversală.
8	Parter P10: compartimentare, mobilier, terasă și proiecția accesului coborât.
9	Etaj V46 rev.7: compartimentare, mobilier, terasă, scara exterioară și rezervele MEP.

Deciziile principale

- Două apartamente independente, unul la parter și unul la etaj, fiecare cu acces propriu și terasă.
- Acces pietonal numai din Dragalina, printr-o poartă de aproximativ 1,10–1,20 m.
- Acces auto numai din Cloșca, prin poartă articulată/segmentată care virează la 90° și se depozitează pe limita vestică.
- Două locuri auto de 2,50 × 5,00 m, orientate perpendicular pe Cloșca.
- Beci tehnic cu acces exterior sub rampa 2; curtea se coboară local la −95 cm pentru un gabarit geometric de aproximativ 203 cm sub podest.
- Subsol la cota provizorie −250 cm, cu vestibul și acces separat la electric/control, apă/termic și depozitare.

Date geometrice de lucru

Parcelă reconstruită	≈145,74 m²; CF indicat 147 m²; valoarea de 172 m² rămâne de lămurit.
Front Dragalina	≈18,54 m, contur ușor neregulat.
Front Cloșca	≈7,93 m.
Amprentă studiată	6,80 × 8,60 m = 58,48 m², înainte de calculul legal POT.
Locuire geometrică	parter ≈38,97 m²; etaj ≈37,88 m²; total ≈76,85 m².
Beci geometric	interior ≈17,64 m²; cu acces exterior ≈21,83 m².

COORDONARE PENTRU ARHITECT

Ce este stabilit și ce trebuie calculat

Accesul pietonal și accesul la beci se întâlnesc într-un mic vestibul exterior din Dragalina, dar traseele se separă imediat. Aleea pietonală trece pe la sudul curții engleze și continuă spre treptele parterului și baza scării etajului. Curtea engleză este protejată cu parapet/balustradă continuă.

Accesul auto

- Deschiderea disponibilă pe Cloșca este aproximativ 7,92 m în geometria de lucru.
- Sistemul trebuie să fie corner sliding: segmente articulate, ghidaj curbat sau soluție echivalentă. Se desenează poziția închisă și poziția retrasă pe limita vestică.
- Furnizorul confirmă numărul segmentelor, raza de curbă, pachetul de stocare, motorul, fotocelulele, evacuarea manuală și comportarea la zăpadă/gheață.
- Cota trotuarului, panta și rigola se coordonează cu șina și garda mașinilor.

Coordonarea construcției

- Se suprapun într-un singur model ridicarea topo, parcela, subsolul S09, parterul P10 și etajul V46 rev.7.
- Secțiunea decisivă traversează curtea −48, curtea engleză −95, podestul +128, scara beciului, peretele parterului și subsolul −250.
- Structuristul verifică fundațiile la limita Dragalina, săpătura subsolului, reazemele scării și posibilitatea eliminării peretelui gros interior.
- Geotehnicul stabilește terenul, apa subterană și sprijinirile. Arhitectul recalculează POT/CUT și toate suprafețele după certificatul de urbanism.
- Planul MEP fixează AC, PRANA, extracția băilor, hota, scurgerile, pantele, tablourile, bateriile, încărcarea auto și degivrarea.

Corecții obligatorii la etaj


- Trei uși glisante în casetă: living–baie, living–dormitor și dormitor–baie; toate coordonate cu instalațiile și mobilierul.
- Golul dormitor–terasă și deplasarea cu 20 cm spre vest rămân de confirmat după alegerea tâmplăriei.
- Prize și iluminat la ambele noptiere, dulap glisant cu adâncime utilă, TV și cabluri în afara casetelor, AC fără jet direct spre pat și PRANA accesibilă pentru curățare.
- Baia: ventilație, hidroizolație, scurgere și pante, oglindă iluminată, suporturi/uscător prosoape și acces la instalații.

Statut: document de concept pentru discuția cu arhitectul. Contururile cadastrale, nivelurile, mecanismul porții, structura și instalațiile trebuie verificate înainte de proiectul pentru autorizare.

CASA DRĂGĂLINA / PLAN GENERAL C01

Amplasament complet: casă, curte, accese și parcare

Nord sus · Dragalina la est/dreapta · Cloșca la sud/jos · contur cadastral reconstruit ≈145,74 m².

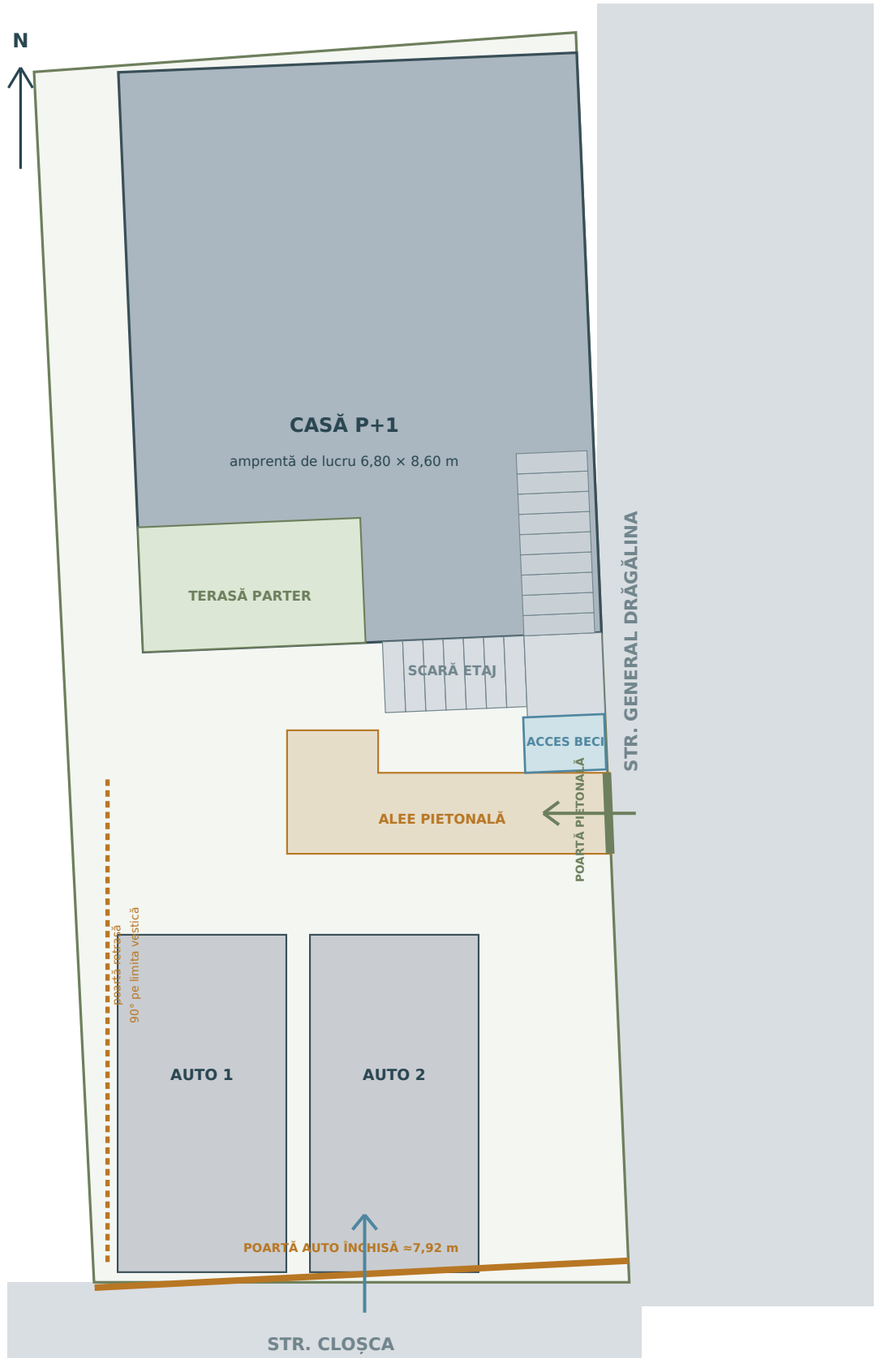

ORGANIZAREA PROPUSĂ

Accesul pietonal este exclusiv din strada General Drăgălina. Poarta de circa 1,20 m intră într-un mic vestibul exterior; traseul se duce spre vest, pe lângă capătul sudic al curții engleze, apoi se separă către parter și scara etajului.

Accesul la beci pornește din același vestibul exterior, dar este controlat separat și coboară spre nord în banda de sub podest/rampa 2. Golul coborât primește parapet sau balustradă continuă față de aleea pietonală.

Accesul auto este exclusiv din strada Cloșca. Sunt păstrate două locuri de parcare de 2,50 × 5,00 m, perpendicular pe front.

Poarta auto închisă urmărește aproape întregul front Cloșca, aproximativ 7,92 m. Deschisă, se retrage la 90° de-a lungul limitei vestice și eliberează aproape tot frontul.

Mecanismul trebuie să fie articulat/segmentat, cu ghidaj în curbă sau soluție echivalentă. O poartă rigidă culisantă nu poate vira la 90°. Se verifică raza, pachetul strâns, automatizarea și evacuarea manuală.

Casa rămâne în jumătatea nordică; curtea sudică păstrează parcarea, banda de manevră, aleea pietonală și accesul la terase/scări.

DATE DE BAZĂ

• Contur cadastral reconstruit: ≈145,74 m²; latura Dragalina ≈18,54 m; latura Cloșca ≈7,93 m.

• Amprentă geometrică de lucru: 6,80 × 8,60 m = 58,48 m² înainte de calculul urbanistic final.

• Spațiu neocupat geometric: ≈87,26 m² înainte de clasificarea teraselor, scărilor, curții engleze și a eventualelor copertine.

CASA DRĂGĂLINA / PLAN GENERAL C01

Detaliu curte sudică: poarta auto la 90°, pietonal și accesul coborât

Nord sus · Dragalina la est/dreapta · Cloșca la sud/jos · contur cadastral reconstruit ≈145,74 m².



CUM FUNCȚIONEAZĂ CURTEA

Poarta Cloșca se deschide complet înaintea manevrei. Cele două mașini intră direct pe locuri, fără a folosi accesul pietonal din Dragalina.

Când poarta este deschisă, segmentele sunt ghidate la 90° și se strâng de-a lungul limitei vestice. Zona de stocare nu trebuie să reducă locul Auto 1 și trebuie protejată față de pietoni.

Poarta pietonală din Dragalina se amplasează la sud de curtea engleză. Astfel persoana intră pe o platformă la nivelul curții, merge spre vest și nu este obligată să traverseze golul coborât.

Din platformă există o ramificație controlată către beci. Parapetul curții engleze continuă până la podest, fără deschideri spre traseul public al oaspeților.

Aleea ajunge la treptele parterului și la baza rampei 1. Accesele celor două apartamente rămân independente după acest punct.

Între capătul parcărilor și zona casei rămâne banda de manevră și circulație; dimensiunea exactă variază cu conturul cadastral și trebuie cotată pe topo.

DE COORDONAT ÎN PROIECT

• Poarta auto: furnizor, număr de segmente, rază de curbă, lungime pachet, șină inferioară sau consolă, motor, fotocelule, deblocare și scurgerea apei.

• Cota trotuarului și panta de acces auto; să nu atingă pragul, șina sau partea inferioară a mașinii.

• Poarta pietonală: sens spre interior, interfon, cutie poștală, iluminat și lățime utilă recomandată de temă ≈1,10–1,20 m.


• Separarea pieton–auto prin material, iluminat și eventual bolarzi; traseu nealunecos și fără praguri periculoase.

• POT/CUT și suprafețele amenajate se calculează de arhitect după certificatul de urbanism și ridicarea topografică.

CASA DRĂGĂLINA / SUBSOL S09

Plan: curte engleză + scară în lungul rampei 2 + vestibul tehnic

Nord sus / sud jos. Variantă cu acces coborât la -95 și camere tehnice cu intrări independente.

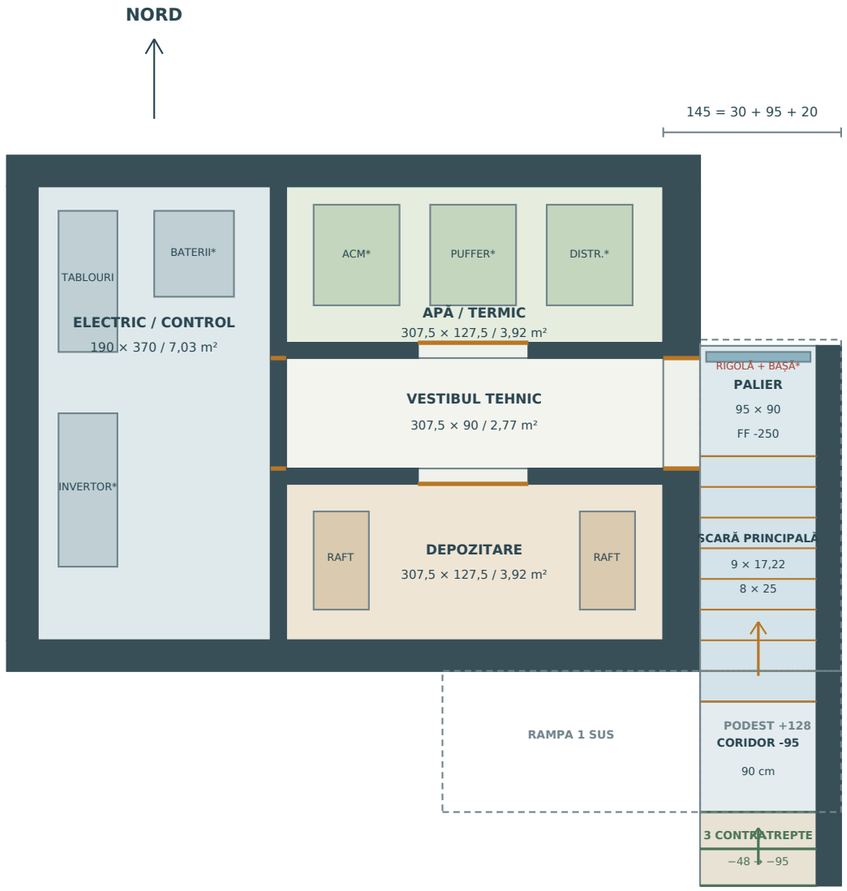

SUPRAFEȚE GEOMETRICE DE LUCRU

Electric/control 7,03 m² · apă/termic 3,92 m² · depozitare 3,92 m²

Camere 14,87 m² · vestibul 2,77 m² · interior beci 17,64 m²

Palier 0,86 m² · rampă 1,90 m² · coridor acces 0,86 m² · trepte exterioare 0,57 m²

Total geometric cu acces: aproximativ 21,83 m². Valoarea utilă/legală se recalculează.

CE REZOLVĂ VARIANTA S09

Curtea se coboară local cu 47 cm: de la -48 la -95, prin trei contratrepte de aproximativ 15,7 cm și două trepte orizontale de 30 cm. Zona coborâtă este numai banda accesului la beci.

Sub podestul +128, cu o structură de lucru de 20 cm, intradosul este aproximativ +108. Față de pardoseala -95 rezultă 203 cm înainte de finisaje; astfel traseul nu mai trece prin zona de 156 cm.

Scara principală coboară de la -95 la -250: nouă contratrepte de aproximativ 17,22 cm și opt trepte de 25 cm. Rampa ocupă 200 cm și ajunge pe palierul 95 × 90 cm.

Palierul este între Y595 și Y685. Peretele sudic al extinderii parterului se termină la Y590; rămâne o rezervă geometrică de 5 cm. Conflictul direct din S08 dispare, dar secțiunea structurală trebuie păstrată.

Din palier intrăm spre vest într-un vestibul tehnic. Electricul, camera de apă/termic și depozitarea au intrări separate din vestibul; nu mai traversăm o cameră pentru a ajunge în alta.

În banda de 145 cm se testează 30 cm perete vestic + 95 cm rezervă de trecere + 20 cm perete estic. Ținta este minimum 90 cm utili după finisaje și mâna curentă; structuristul confirmă peretele estic.

CONDIȚII OBLIGATORII

• Rigolă la baza scării, bașă și pompă dacă evacuarea gravitațională nu este posibilă; hidroizolație continuă și prag ridicat la ușa care se deschide spre vestibul.


• Balustradă/mână curentă fără reducerea lățimii utile sub ținta stabilită; iluminat exterior și suprafețe antiderapante.

• Echipamentele desenate sunt rezerve. Încăperile se confirmă după lista de produse, distanțele de service, ventilație și transport.

CASA DRĂGĂLINA / SUBSOL S09

Secțiune S–S: gabarit continuu din curte până la palierul subsolului

Nord sus / sud jos. Variantă cu acces coborât la -95 și camere tehnice cu intrări independente.

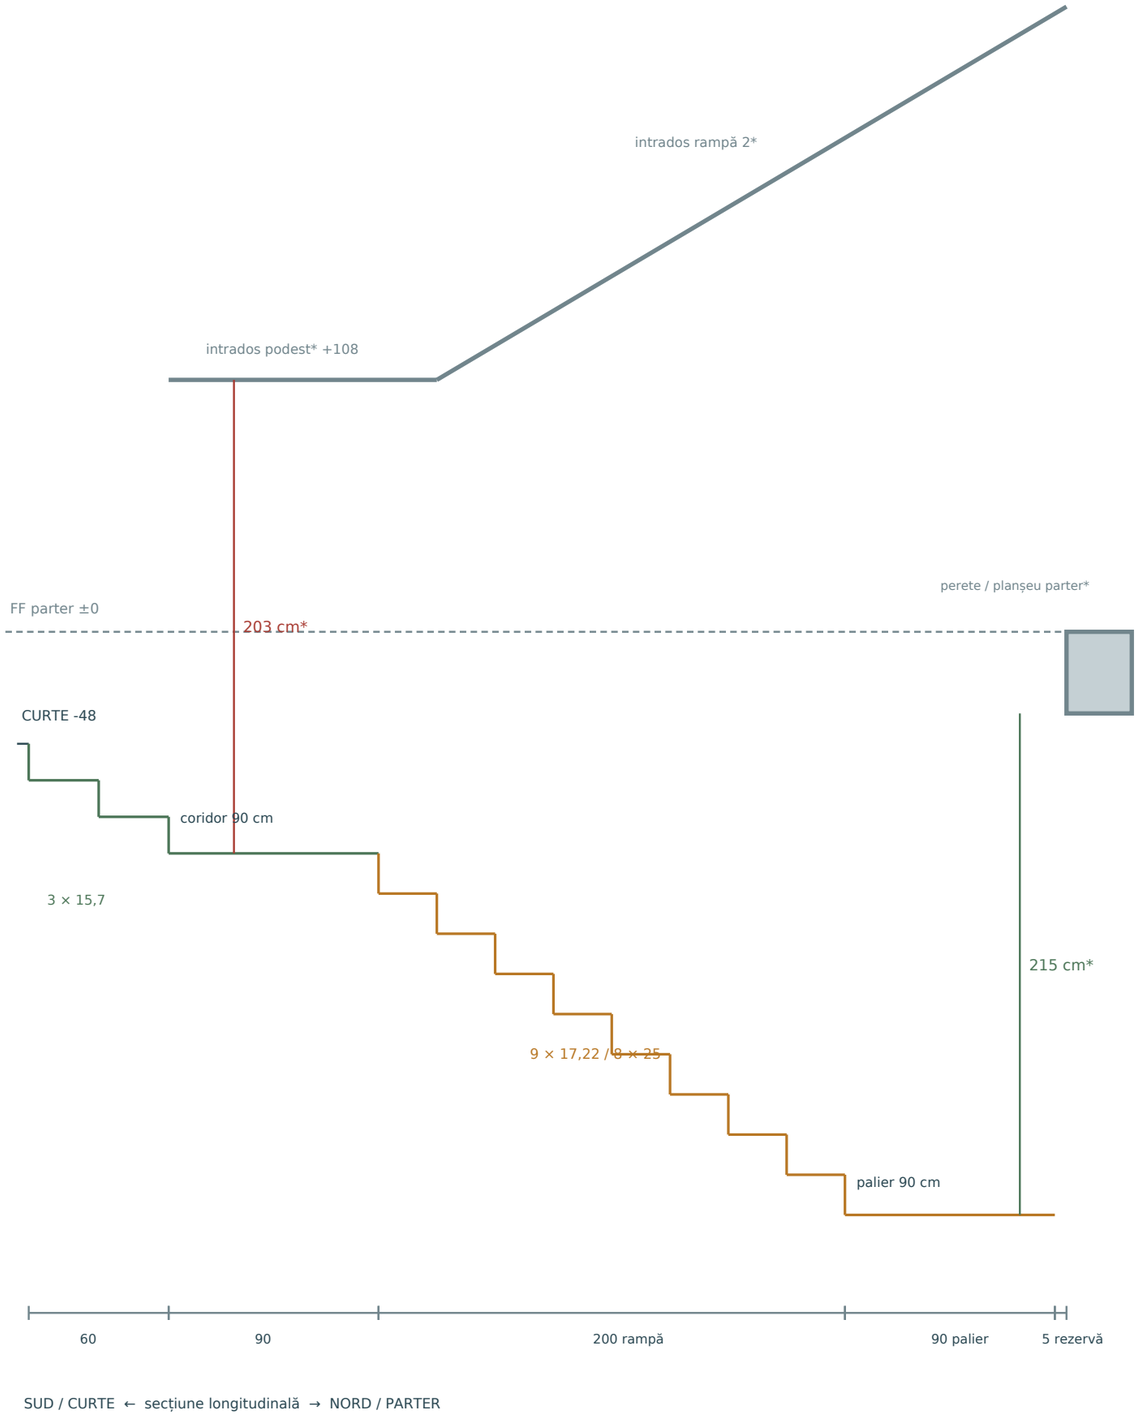

SUD / CURTE ← secțiune longitudinală → NORD / PARTER

VERIFICAREA GABARITULUI

Punctul critic este coridorul de sub podest. Pardoseala -95 și intradosul estimat +108 dau 203 cm geometric. În proiect se stabilește gabaritul finit după structură, tencuieli, corpuri de iluminat și eventuale grinzi.

Ușa de siguranță se amplasează la baza scării și se deschide spre vestibul, nu peste palier. Coridorul superior poate rămâne deschis, protejat de podest, cu control de acces la ușa de jos.

După limita podestului, scara de deasupra urcă iar scara de beci coboară; înălțimea liberă crește. Nu mai folosim valoarea idealizată de 484,2 cm din S08, deoarece nu reprezenta plafonul real al încăperilor.

Palierul se încheie la 5 cm înaintea proiecției peretelui parterului. Această rezervă este numai geometrică: arhitectul și structuristul trebuie să coteze fundația, grinda, rostul și hidroizolația.

Pentru camere se urmăresc minimum 210 cm finit până la cel mai jos element permanent. Cu FF -250 și un intrados de lucru -35 rezultă 215 cm geometric, adică o rezervă de circa 5 cm.

COTE PROVIZORII

• Curte generală -48 · curte engleză/coridor -95 · subsol -250 · parter ±0 · podest scară etaj +128 · etaj +288.


• Diferența coridor–subsol este 155 cm. Diferența totală curte–subsol este 202 cm, împărțită în 47 cm exterior + 155 cm scara principală.

• Dacă structura cere un intrados mai jos de -35, pardoseala subsolului se coboară corespunzător sau se acceptă o înălțime mai mică numai după verificarea cerințelor aplicabile.

CASA DRĂGĂLINA / SUBSOL S09

Secțiune A–A: bandă de 145 cm, apă și detaliu de acces

Nord sus / sud jos. Variantă cu acces coborât la -95 și camere tehnice cu intrări independente.

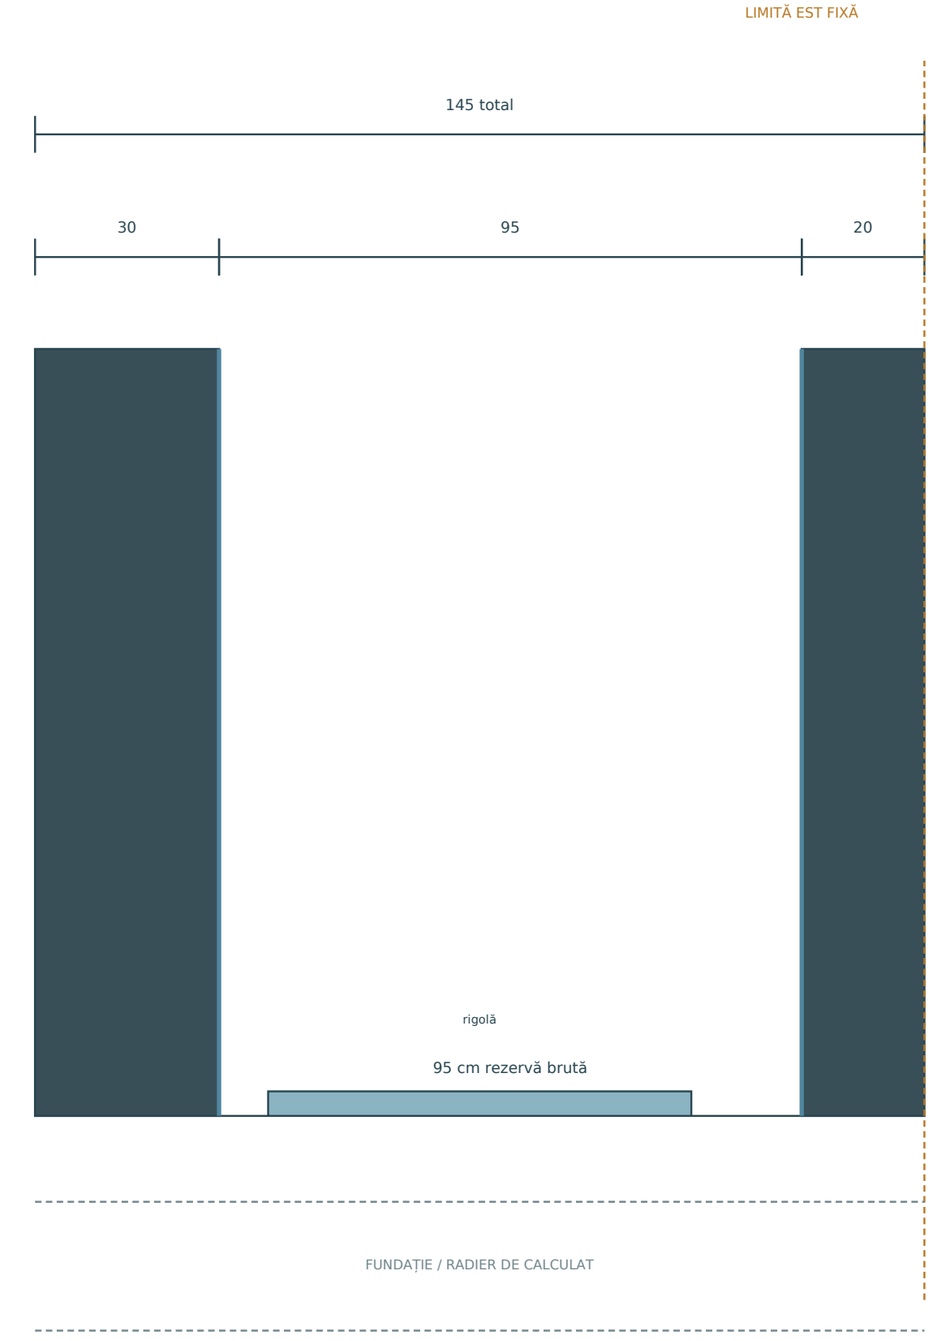

Țintă: minimum 90 cm utili după finisaje și mână curentă.

Secțiune schematică 1:10 · pereții de 30/20 cm sunt rezerve, nu dimensionare structurală.

CERINȚE PENTRU ARHITECT ȘI SPECIALIȘTI

Păstrați fața exterioară estică în limita de proprietate. Hidroizolația, protecția și soluția de fundare trebuie proiectate fără depășirea acesteia; nu se presupune o talpă simetrică.

Confirmați dacă peretele estic de 20 cm este posibil structural. Dacă trebuie îngroșat, lățimea se ia spre vest sau se ajustează conturul interior; ținta de 90 cm utili nu se reduce fără o decizie explicită.

Curtea engleză primește pante spre rigolă, hidroizolație continuă, protecție la îngheț și finisaj antiderapant. Evacuarea apei se proiectează inclusiv pentru o ploaie intensă și defectarea pompei.

Ușa dintre palier și vestibul se cotează pentru introducerea celui mai mare echipament. Se recomandă gol util de 90 cm dacă geometria și cerințele de foc permit.

Camera electrică se separă de apă și are acces direct din vestibul. Tipul bateriilor, invertoarelor și tablourilor determină ventilația, distanțele, detecția și alcătuirea pereților/ușii.

Camera de apă/termic are sifon de pardoseală, ventilație și acces la vane. Depozitarea nu trebuie să blocheze tablourile, pompele sau traseul de evacuare.

Se face studiu geotehnic și proiect de sprijinire a săpăturii, inclusiv efectul asupra vecinătăților și asupra scării exterioare. Fundația nu se deduce din grosimea pereților.

STATUS DUPĂ REVIZIE

• Rezolvat geometric: traseul de 156 cm este eliminat; palierul nu mai intră sub peretele parterului; camerele au acces independent.

• De confirmat prin proiect: structura podestului, cota exactă -95, nivelul -250, lățimea netă, fundațiile, drenajul și lista echipamentelor.

• S09 înlocuiește S08 ca variantă recomandată de studiu.

CASA DRAGALINA / PARTER P10

Nord sus, sud jos / primire separată de bucătărie / acces beci sub rampa 2

Scara 1:50 pe A3 / tipărire 100%. Cote în cm. Variantă de studiu, nu soluție validată.



PARTER COORDONAT CU SUBSOLUL

Intrare în apartament din terasa vestică, spre zona de primire; nu direct în bucătărie. Deschidere pe dreapta privind spre apartament. Cuier cu agățători în spatele foii, fără dulap acolo; corp de depozitare opus de 130 × 30 cm, h90. Ușă cu vitrare sau luminator de ales.

Bucătărie pe nord: front 290 cm, module 60 FR + 60 MSV + 60 chiuvetă + 60 plită/cuptor + 50 blat. Modelul aparatelor, hota, fronturile deschise și blatul real se coordonează.

Dining: masă Ø100, patru scaune. Canapea pe est 90 × 170, la 10 cm de perete; probă desfăcută spre vest 180 × 170. TV pe vest, măsuță mobilă 40 × 40. Traseu geometric de 92 cm cu TV+suport 8 cm, înainte de dublaje.

Preluăm în apartament zona de sub platforma etajului: rezervă geometrică 115 × 120 = 1,38 m². Segmentul fostului perete exterior devenit interior se elimină numai după verificarea structurii, reazemelor platformei și scării.

Accesul la beci urmează varianta S09. În banda estică, curtea coboară local de la -48 la -95 prin trei contratrepte de circa 15,7 cm și două trepte de 30 cm. Urmează un coridor de 90 cm sub podest și scara principală spre nord.

Scara principală coboară de la -95 la -250 prin 9 contratrepte de circa 17,22 cm și 8 trepte de 25 cm. Palierul este Y595-685, complet la sud de peretele parterului care începe la Y590. Banda de 145 cm testează 30 perete + 95 rezervă scară + 20 perete estic.

Curte -48 față de parter. Cele două suprafețe exterioare de treaptă desenate la sud sunt la -32 și -16, apoi urcarea la terasa ±0: trei contratrepte de 16, două trepte orizontale de 30. Nu extindem conturul dincolo de Y1035.

Terasă acoperită și neacoperită unite. Fără poartă și fără umbrelă desenată. Parapet și paravan de intimitate lângă accesul cu trepte, continuate până în dreptul intrării; golul de acces la apartament rămâne liber.

Dormitor și baie: geometria P08 păstrată. Acces living-baie și living-dormitor cu uși în casetă; acces dormitor-baie desenat batant ca rezervă, de comparat cu preferința pentru glisare în perete. Nu considerăm caseta rezolvată.

Anvelopa, casetele, TV, AC, PRANA, instalațiile băii, electricul și traseele spre beci se dezvoltă conform temei din paginile introductive. Suprafețele sunt geometrice, nu un calcul legal final.

PUNCTE DE COORDONAT


• Verificați în aceeași secțiune curtea -48, zona coborâtă -95, podestul +128, scara etajului, scara beciului și fundațiile. Gabaritul geometric sub podest este circa 203 cm înainte de finisaje.

• Rigolă, bașă/pompă, hidroizolație, prag și protecția la îngheț sunt obligatorii pentru accesul exterior coborât. Ușa de jos se deschide spre vestibul.

• TV, canapea extinsă, scaune ocupate/retrase, haine pe cuier și accesul la sertare trebuie verificate cu produse reale.

V46 rev.7 · etaj (același footprint P+1 — rezerve coloane)

util geom. 37.8787 m² · baie net ~6.53 · terasă liberă 16.09 · V45 păstrat

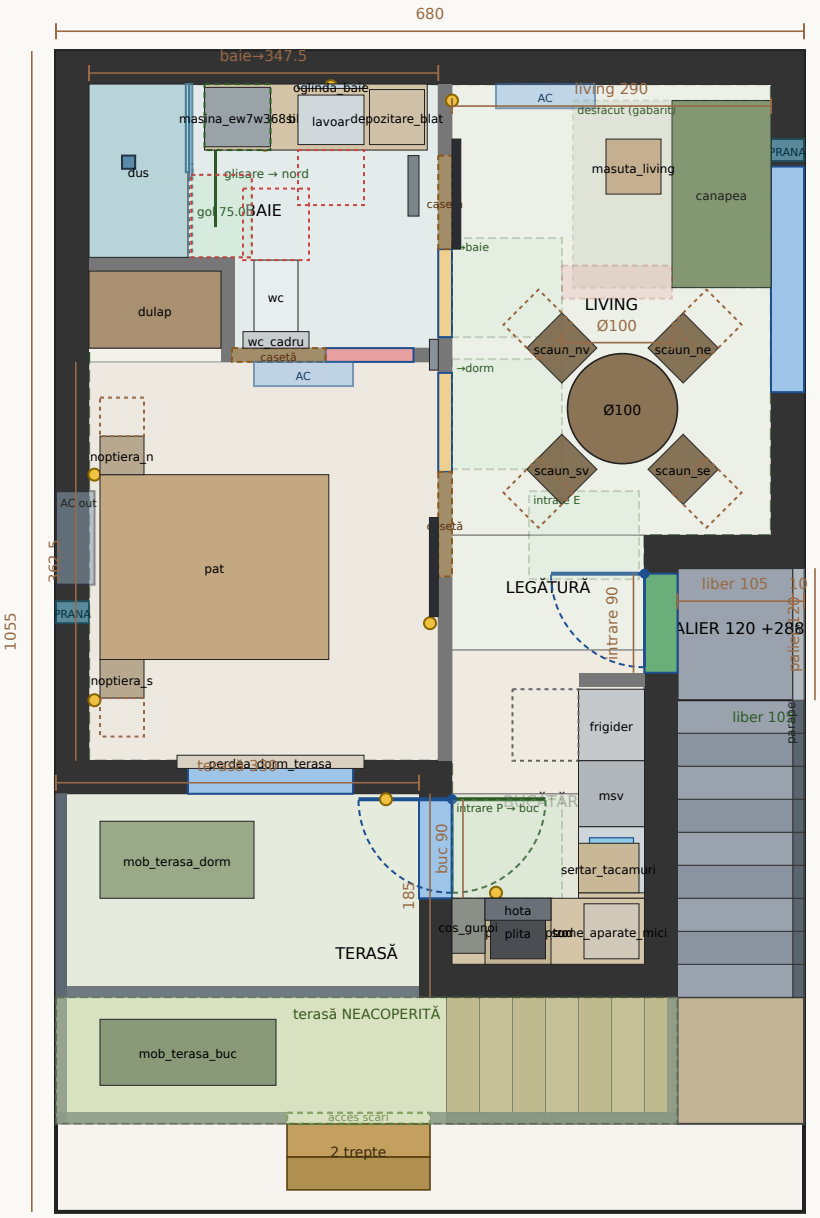

V46 rev.7

Util geom.: 37.8787 m²

- P: intrare pe buc–terasă
- P: terasă mărită + neacop.
- E: intrare pe scară (est)
- TV centrate + întărire
- AC out = fațadă VEST
- Dining →dorm 68 occ.
- Urbanism terasă: deschis
- Alcătuiri NECONFIRMATE